
ML/B01AM ATRIUM

INTERFACES OF SYSTEM 07 ONLY - INTERNAL WIRING: DWG 006376A6F41026002

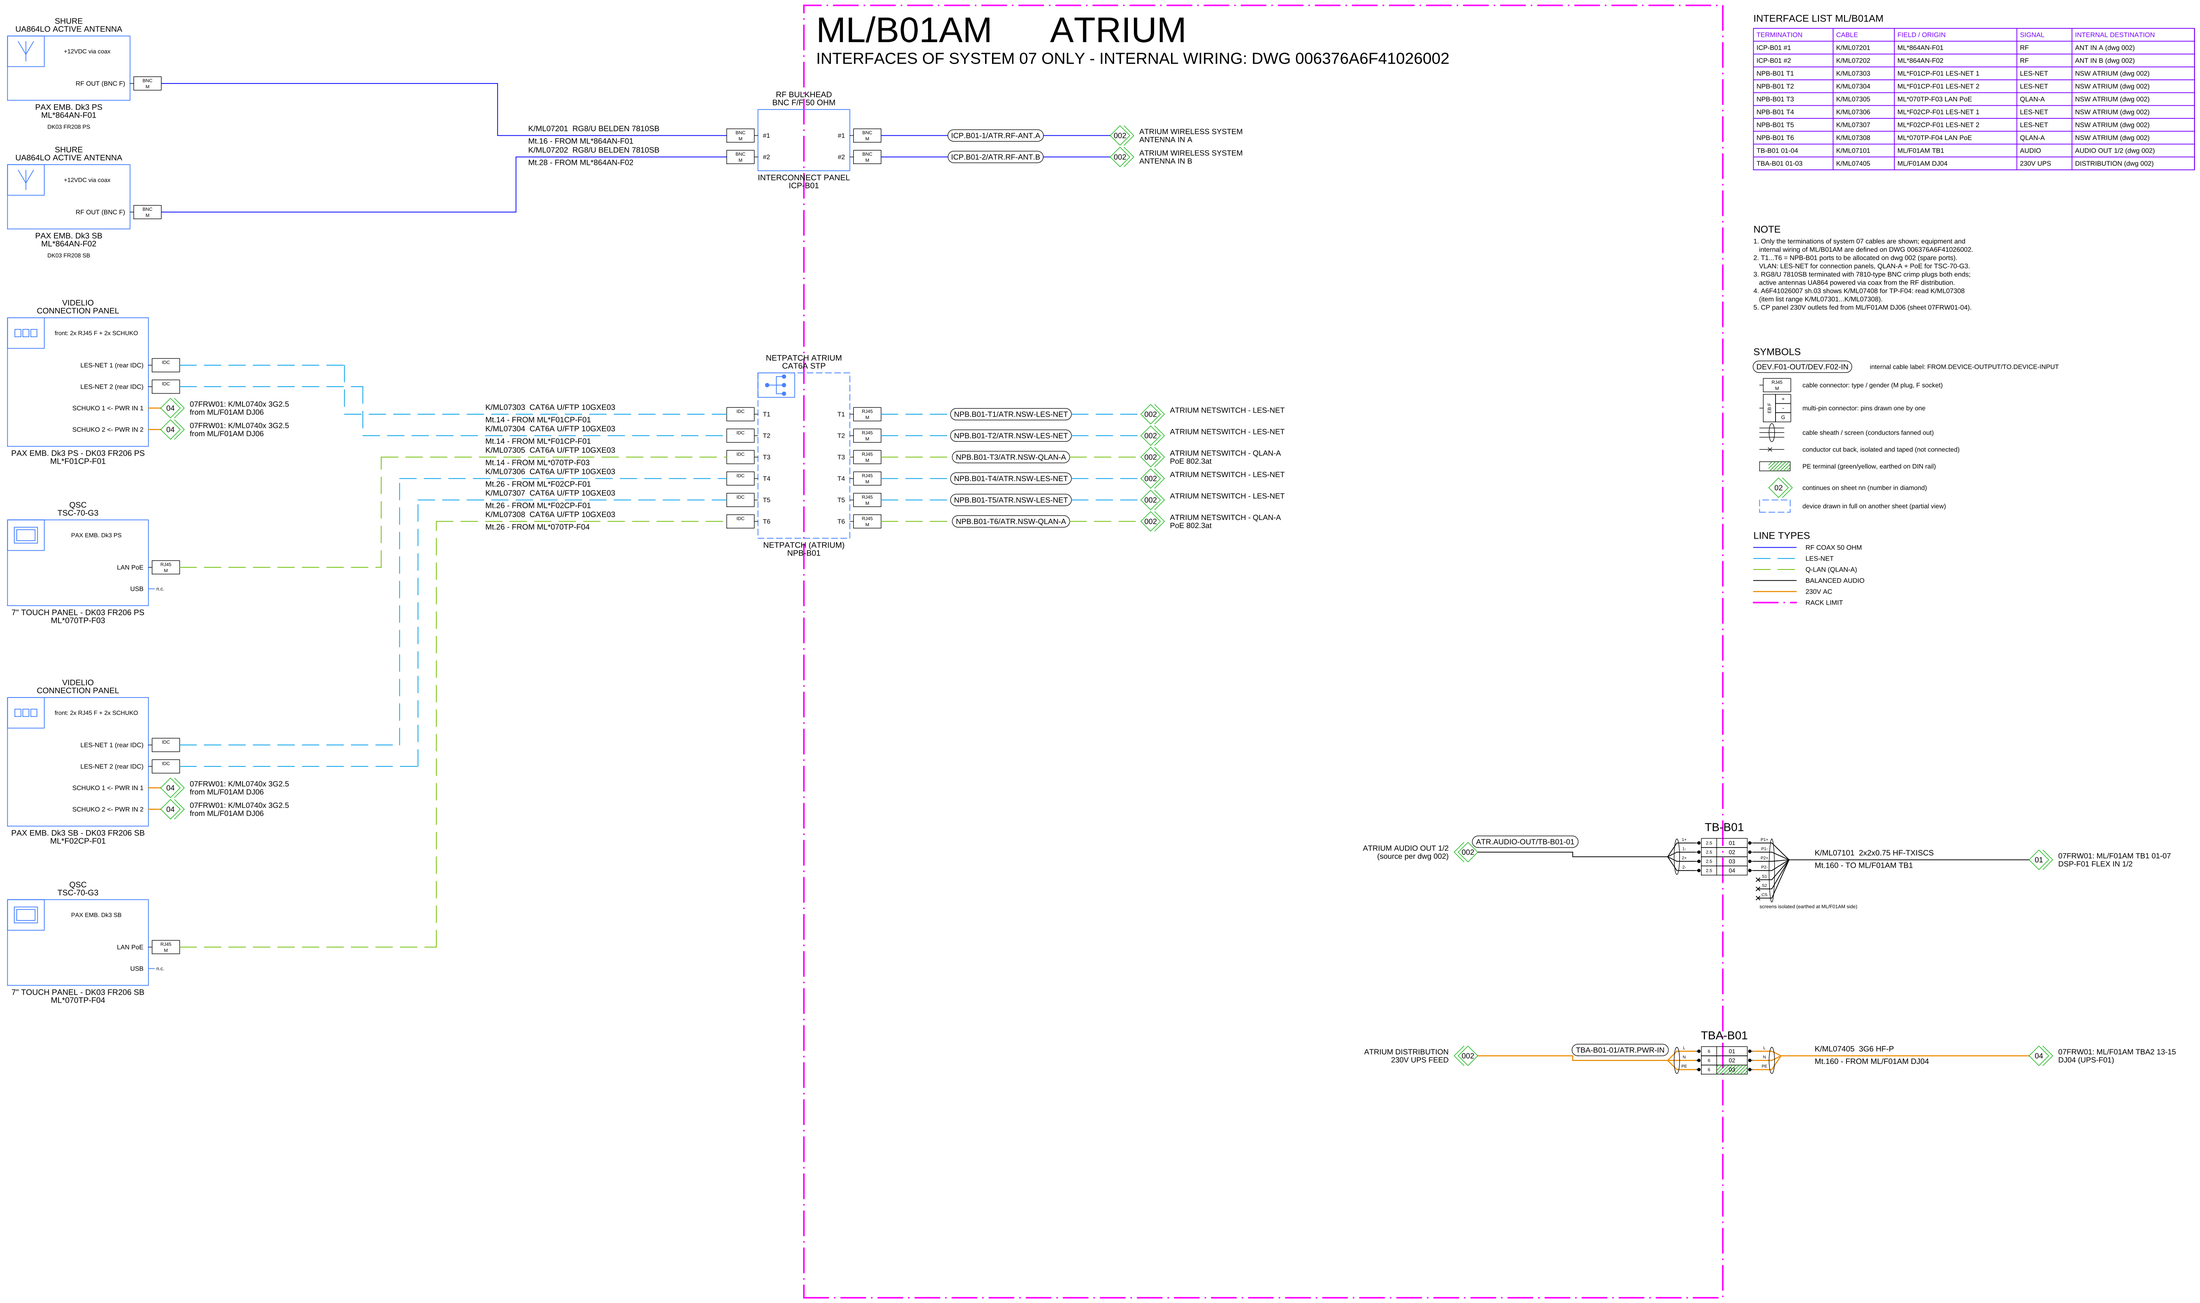

INTERFACE LIST ML/B01AM

TERMINATION	CABLE	FIELD / ORIGIN	SIGNAL	INTERNAL DESTINATION
ICP-B01 #1	K/ML07201	ML*864AN-F01	RF	ANT IN A (dwg 002)
ICP-B01 #2	K/ML07202	ML*864AN-F02	RF	ANT IN B (dwg 002)
NPB-B01 T1	K/ML07303	ML*F01CP-F01 LES-NET 1	LES-NET	NSW ATRIUM (dwg 002)
NPB-B01 T2	K/ML07304	ML*F01CP-F01 LES-NET 2	LES-NET	NSW ATRIUM (dwg 002)
NPB-B01 T3	K/ML07305	ML*070TP-F03 LAN PoE	QLAN-A	NSW ATRIUM (dwg 002)
NPB-B01 T4	K/ML07306	ML*F02CP-F01 LES-NET 1	LES-NET	NSW ATRIUM (dwg 002)
NPB-B01 T5	K/ML07307	ML*F02CP-F01 LES-NET 2	LES-NET	NSW ATRIUM (dwg 002)
NPB-B01 T6	K/ML07308	ML*070TP-F04 LAN PoE	QLAN-A	NSW ATRIUM (dwg 002)
TB-B01 01-04	K/ML07101	ML/F01AM TB1	AUDIO	AUDIO OUT 1/2 (dwg 002)
TBA-B01 01-03	K/ML07405	ML/F01AM DJ04	230V UPS	DISTRIBUTION (dwg 002)

NOTE

1. Only the terminations of system 07 cables are shown; equipment and internal wiring of ML/B01AM are defined on DWG 006376A6F41026002.
2. T1..T6 = NPB-B01 ports to be allocated on dwg 002 (spare ports).
   VLAN: LES-NET for connection panels, QLAN-A + PoE for TSC-70-G3.
3. RG8/U 7810SB terminated with 7810-type BNC crimp plugs both ends; active antennas UA864 powered via coax from the RF distribution.
4. A6F41026007 sh.03 shows K/ML07408 for TP-F04: read K/ML07308 (item list range K/ML07301..K/ML07308).
5. CP panel 230V outlets fed from ML/F01AM DJ06 (sheet 07FRW01-04).

SYMBOLS

DEV.F01-OUT/DEV.F02-IN — internal cable label: FROM.DEVICE-OUTPUT/TO.DEVICE-INPUT

RJ45 M — cable connector: type / gender (M plug, F socket)

DB-9 F — multi-pin connector: pins drawn one by one

cable sheath / screen (conductors fanned out)

conductor cut back, isolated and taped (not connected)

PE terminal (green/yellow, earthed on DIN rail)

02 — continues on sheet nn (number in diamond)

device drawn in full on another sheet (partial view)

LINE TYPES

- RF COAX 50 OHM
- LES-NET
- Q-LAN (QLAN-A)
- BALANCED AUDIO
- 230V AC
- RACK LIMIT

videlio HMS Videlio HMS Italy srl via G. Deledda 3, 34079 Staranzano (GO)	Client / Shipyard: FINCANTIERI S.p.A. CRYSTAL CRUISES - HULL 6376	Project: HULL 6376	Drawing No: 07BRW01	Area: 07 - CREW & OFFICER MESS ML/B01AM - DK04 FR149 SB CABINET (ATRIUM)	System: L.E.S. WIRING DIAGRAM RACK ML/B01AM (ATRIUM) INTERFACES OF SYSTEM 07 - CREW & OFFICER MESS	Sheet: 01 / 01	Rev.	Date	Description	Drawn	Appr.	Print: A1	Date: 30/10/2026	COPYRIGHT, REPRODUCTION AND/OR DISCLOSURE IS FORBIDDEN WITHOUT VIDELIO HMS WRITTEN AUTHORIZATION
							A	30/10/2026	FIRST ISSUE - EXECUTIVE WIRING (from 006376A6F41026007 rev.00)			Scale: N.T.S.	Drawn by:	Ref.: 006376A6F41026007 rev.00
													Approved:	