


ML/B01AM ATRIUM

SYSTEM 07 INTERFACES ONLY - INTERNAL WIRING: DWG 006376A6F41026002

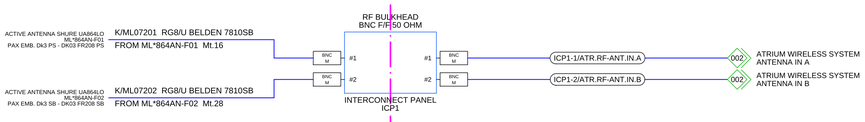

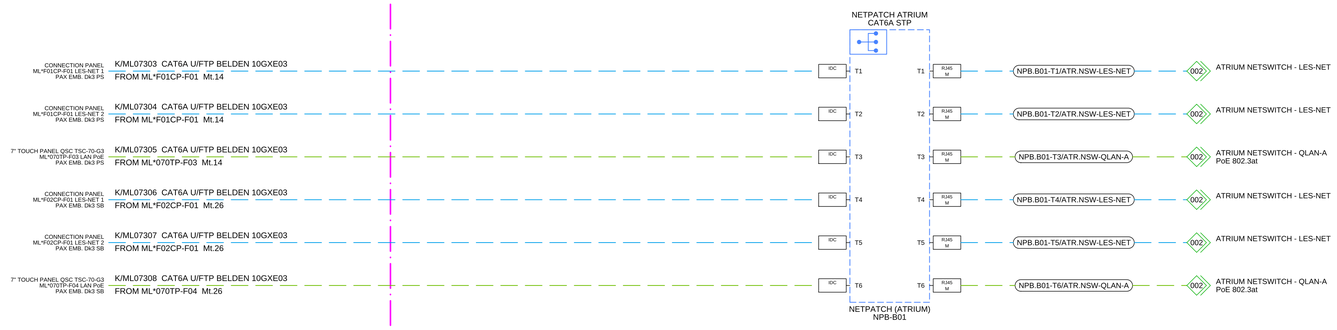

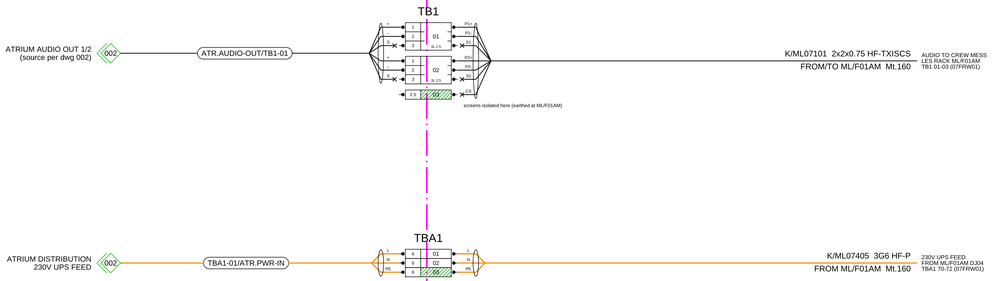

INTERFACE LIST ML/B01AM

TERMINATION	CABLE	FIELD / ORIGIN	SIGNAL	INTERNAL DESTINATION
ICP1 #1	K/ML07201	ML*864AN-F01	RF	ANT IN A (dwg 002)
ICP1 #2	K/ML07202	ML*864AN-F02	RF	ANT IN B (dwg 002)
NPB-B01 T1	K/ML07303	ML*F01CP-F01 LES-NET 1	LES-NET	NSW ATRIUM (dwg 002)
NPB-B01 T2	K/ML07304	ML*F01CP-F01 LES-NET 2	LES-NET	NSW ATRIUM (dwg 002)
NPB-B01 T3	K/ML07305	ML*070TP-F03 LAN PoE	QLAN-A	NSW ATRIUM (dwg 002)
NPB-B01 T4	K/ML07306	ML*F02CP-F01 LES-NET 1	LES-NET	NSW ATRIUM (dwg 002)
NPB-B01 T5	K/ML07307	ML*F02CP-F01 LES-NET 2	LES-NET	NSW ATRIUM (dwg 002)
NPB-B01 T6	K/ML07308	ML*070TP-F04 LAN PoE	QLAN-A	NSW ATRIUM (dwg 002)
TB1 01-03	K/ML07101	ML/F01AM TB1	AUDIO	AUDIO OUT 1/2 (dwg 002)
TBA1 01-03	K/ML07405	ML/F01AM DJ04	230V UPS	DISTRIBUTION (dwg 002)

NOTE

1. Only the terminations of system 07 cables are shown; equipment and internal wiring of ML/B01AM: DWG 006376A6F41026002.
2. T1...T6 = NPB-B01 spare ports to be allocated on dwg 002.
   VLAN: LES-NET connection panels, QLAN-A + PoE TSC-70-G3.
3. RG8/U 7810SB: 7810-type BNC crimp plugs both ends.
4. TB1: 3-level signal terminals; TBA1: 1-level power terminals.
5. A6F41026007 sh.03 K/ML07408 read as K/ML07308.
6. CP panel 230V outlets fed from ML/F01AM DJ06 (07FRW01).

SYMBOLS

DEV.F01-OUT/DEV.F02-IN — internal cable label: FROM.DEVICE-OUTPUT/TO.DEVICE-INPUT

- cable connector: type / gender (M plug, F socket)
- multi-pin connector: pins drawn one by one
- cable sheath / screen (conductors fanned out)
- conductor cut back, isolated and taped (not connected)
- PE terminal (green/yellow, earthed on DIN rail)
- 02 — continues on sheet nn (number in diamond)
- device drawn in full on another sheet (partial view)

LINE TYPES

- RF COAX 50 OHM
- LES-NET
- Q-LAN (QLAN-A)
- BALANCED AUDIO
- 230V AC
- RACK LIMIT

videlio HMS Videlio HMS Italy srl via G. Deledda 3, 34079 Staranzano (GO)	Client / Shipyard: FINCANTIERI S.p.A. CRYSTAL CRUISES - HULL 6376	Project: HULL 6376	Drawing No: 07BRW01	Area: 07 - CREW & OFFICER MESS ML/B01AM - DK04 FR149 SB CABINET (ATRIUM)	System: L.E.S. RACK WIRING DIAGRAM RACK ML/B01AM (ATRIUM) INTERFACES OF SYSTEM 07 - CREW & OFFICER MESS	Sheet: 01 / 01	Print: A1	Scale: N.T.S.	Date: 30/10/2026	Drawn by:	Approved:

Rev.	Date	Description	Drawn	Appr.
A	30/10/2026	FIRST ISSUE - EXECUTIVE WIRING (from 006376A6F41026007 rev.00)		

COPYRIGHT, REPRODUCTION AND/OR DISCLOSURE IS FORBIDDEN WITHOUT VIDELIO HMS WRITTEN AUTHORIZATION

Ref.: 006376A6F41026007 rev.00